



① 正面立面図（道路側より見る）

S = NTS（形状・寸法は現地実測による）

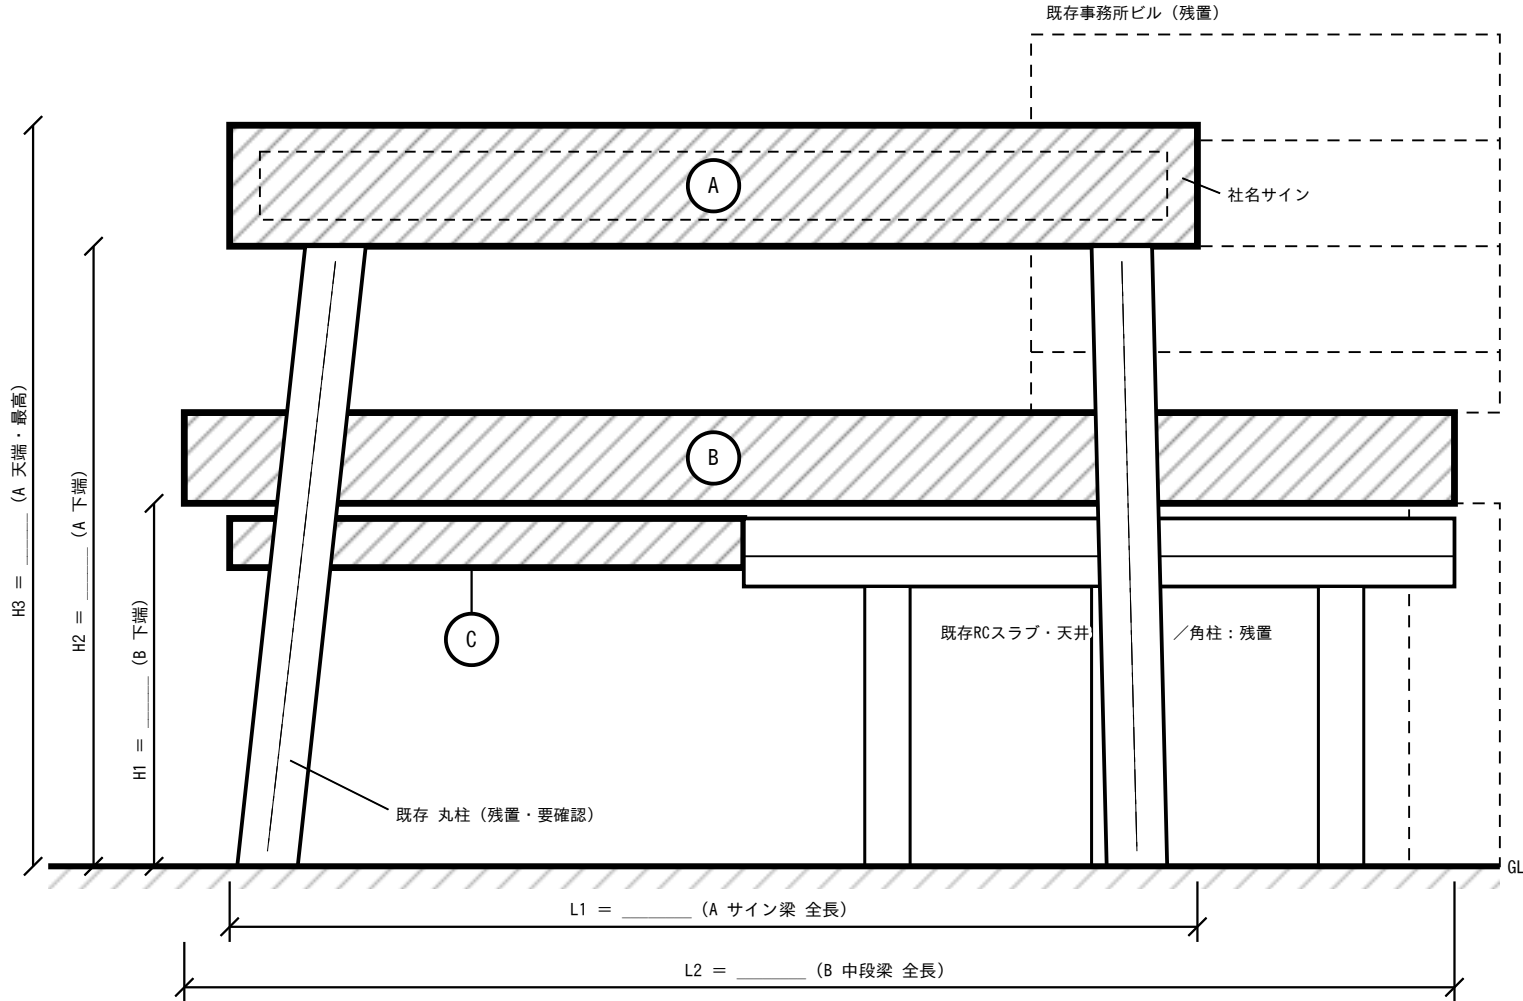


② 側面図（ポリカ屋根部で切る）

S = NTS

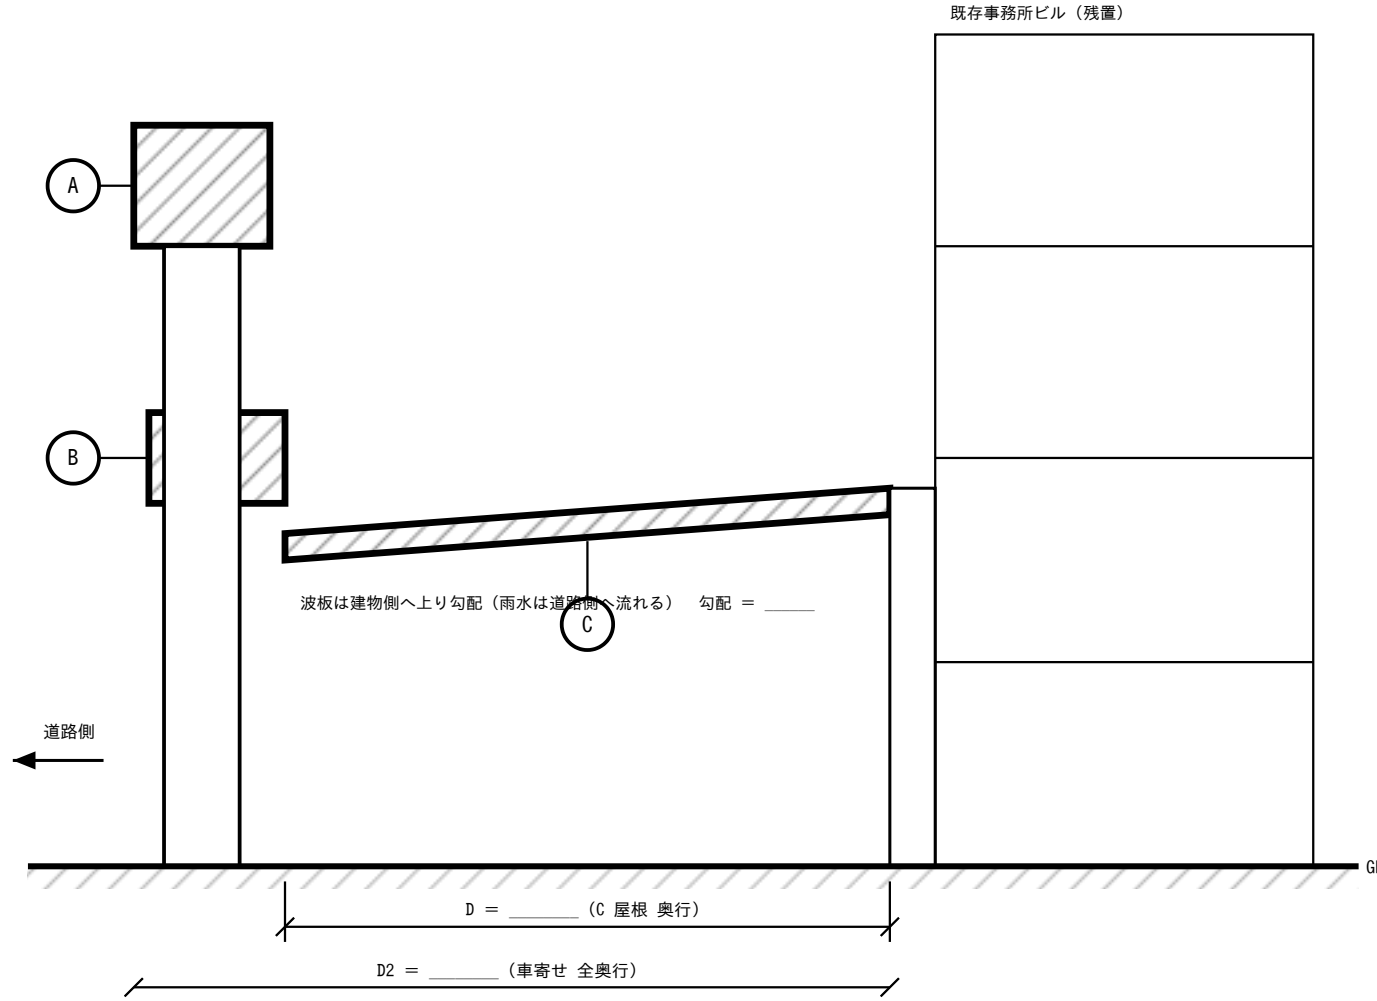

③ 車寄せ 屋根伏図（撤去範囲）

S = NTS

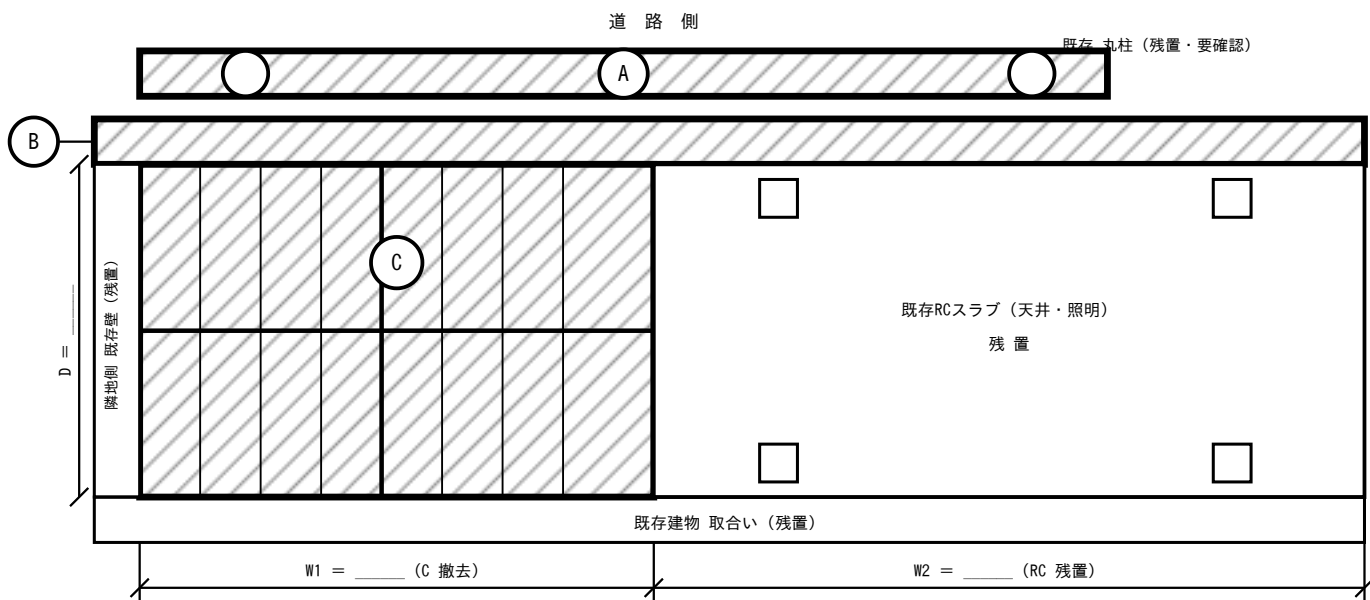

※ C：ポリカ波板 = 2スパン（中央に小梁）×前後2列。割付 ____ 枚、母屋ピッチ ____、板厚 ____ を現地確認。

※ 写真①（見上げ）のマーキング範囲=この C の部分。

注 記

- 本図は現地写真をもとに作成した略図。形状・寸法・スパン割は現地実測により確定する。
- 撤去範囲 = A：社名サイン付き上部梁／B：中段 大梁／C：車寄せ 採光屋根（ポリカ波板＋母屋）。
- B（中段梁）は構造体。切断範囲・順序・仮支持（サポート）を検討。梁のみ撤去時は残る丸柱の安定を確認。
- サイン内部の照明・電源配線、屋根下の照明・配線の切離しを事前に行う。
- 高所作業（A 天端 H≒7m 想定）。高所作業車／足場、道路使用・歩道養生、営業中の車両移動を確認。
- 石綿含有建材（成形板・シーリング等）の事前調査結果を確認のうえ着手。撤去材は分別・積込・搬出・処分。

④ 撤去範囲リスト

記号	撤去部位	仕様・材質（想定）	数量（実測記入）	備 考
A	社名サイン付き 上部梁 （門型 頂部・両端はね出し共）	鋼製サイン板＋梁 板金・化粧板巻き	L = ____ m H = ____ m	サイン内 照明・配線の切離し 高所作業車 必要（H≒7m）
B	中段 大梁（門型 中段） 左右はね出し部を含む	RC／鉄骨＋板金・化粧板 錆汁・欠損・鉄筋露出あり	L = ____ m H = ____ m	構造体：切断範囲・仮支持を検討 RCスラブとの取合い切断位置
C	車寄せ 採光屋根 （ポリカ波板＋鋼製母屋・小梁）	ポリカ波板 t = ____ 鋼製母屋・アングル	W ____ × D ____ = ____ m ² （ ____ 枚）	直下の駐車車両 移動・養生 撤去後の雨仕舞い・端部処理
残置	既存RCスラブ（天井・照明） 角柱・門型 丸柱・隣地側 既存壁	—	—	丸柱の存置／撤去はお客様と確認 残置部の養生・仕上げ復旧の要否

凡 例



撤去範囲（A・B・C）

—— 既存・残置部

- - - - 後方・見え掛り／不明部

※ 太線＋斜線ハッチ = 撤去、細線 = 残置。切断位置は現地で墨出し・写真記録のこと。

現調メモ（実測・所見）

撤 去 範 囲 図（現地調査用）

工事名	車寄せ サイン梁・中段梁・採光屋根 撤去工事（仮称）		
所在地	神奈川県横浜市都筑区茅ヶ崎南 3-23-5		
建 物	信和ホームズ㈱ 社屋 車寄せ（写真サイン表記による）		
現調日 2026/09/02（水）9:00		作成日 2026/09/01	
縮尺 NTS	用紙 A3	図番 01（rev.1）	