


### ① 正面図（道路側より見る）

S = NTS（形状・寸法は現地実測による）

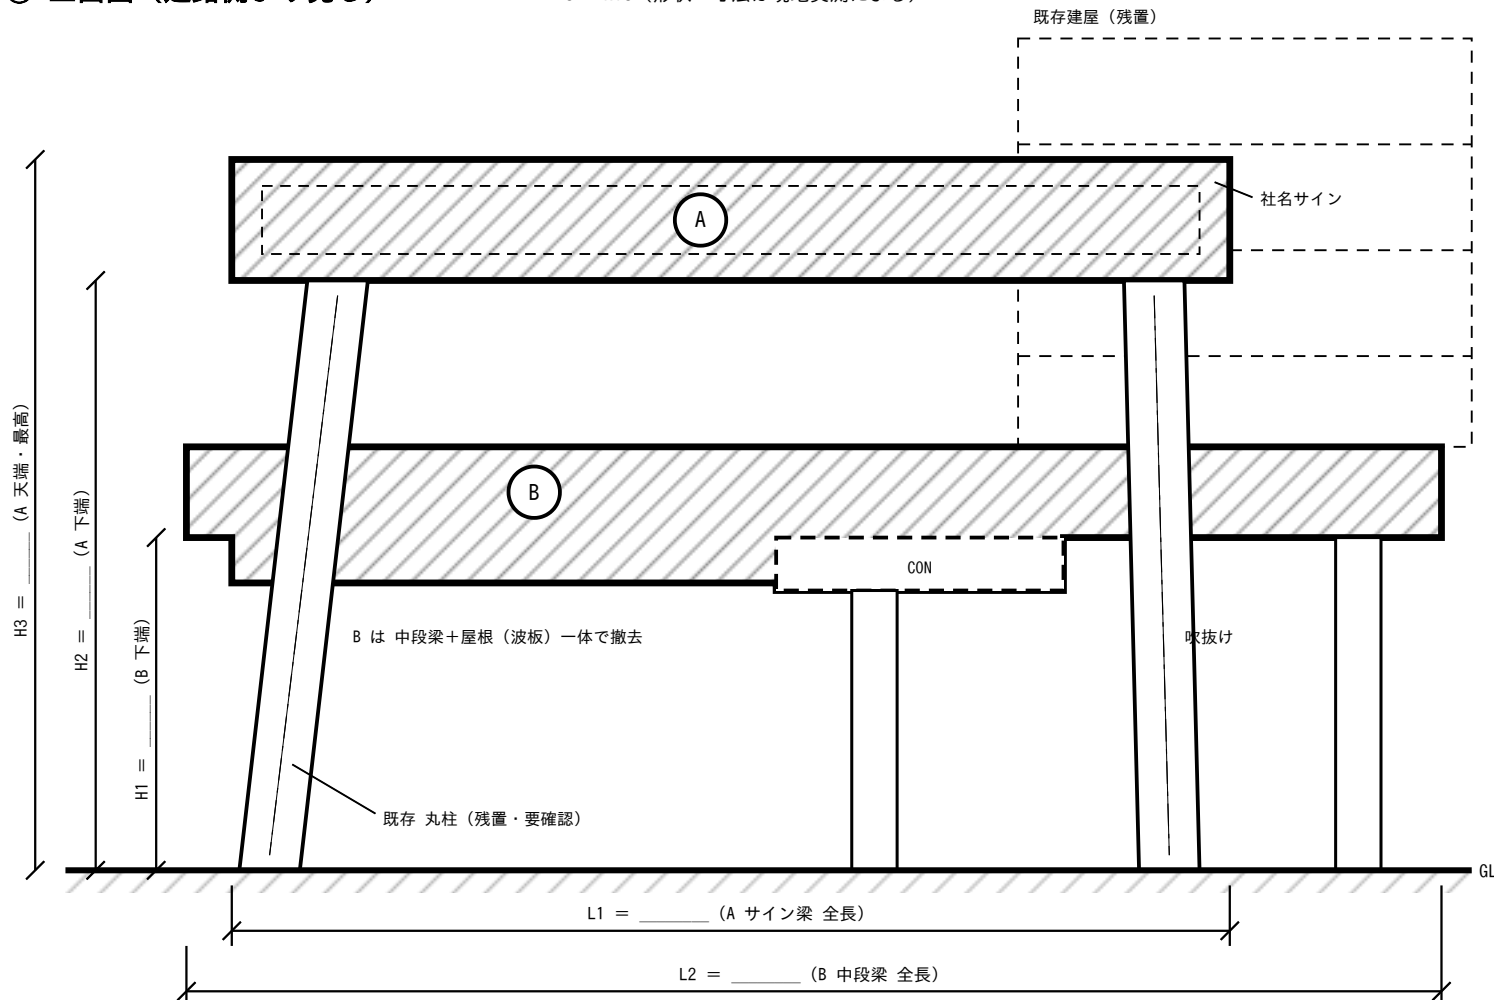


※ 丸柱・角柱・既存建屋は残置。CON 部の撤去要否は現地確認（②参照）。

### ③ 撤去範囲リスト

| 記号  | 撤去部位                                      | 仕様・材質（想定）                | 数量（実測記入）                               | 備 考                                 |
|-----|-------------------------------------------|--------------------------|----------------------------------------|-------------------------------------|
| A   | 社名サイン付き 上部梁<br>（門型 頂部・はね出し共）              | 鋼製サイン板＋梁<br>板金・化粧板巻き     | L = ____ m<br>H = ____ m               | サイン内 照明・配線の切離し<br>高所作業車 必要（H≧7m）    |
| B   | 中段梁 ＋ 屋根 一体<br>（波板／ルーバー部を含む）              | 鋼製梁＋ポリカ波板<br>鋼製・アルミ ルーバー | L = ____ m<br>面積 = ____ m <sup>2</sup> | 構造体：切断範囲・順序・仮支持を検討<br>直下の駐車車両 移動・養生 |
| 要確認 | CON 部（RCスラブ）／ルーバー部の撤去要否<br>門型 丸柱・角柱の存置／撤去 | RC スラブ・天井・照明<br>—        | ____ m <sup>2</sup><br>—               | 現地でお客様と範囲確定のうえ図面へ朱書き<br>吹抜け部は撤去なし   |

#### 凡 例

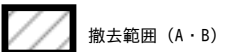

撤去範囲（A・B）



撤去要否 要確認

—— 既存・残置部

- - - - 後方

※ 太線＋斜線ハッチ = 撤去。切断位置は現地で墨出し・写真記録のこと。


#### 注 記

- 本図は現地写真および手描きスケッチをもとに作成した略図。寸法・範囲は現地実測により確定する。
- 撤去範囲＝ A：社名サイン付き上部梁／B：中段梁＋屋根（波板・ルーバー部）一体。
- B は構造体。切断範囲・順序・仮支持（サポート）を検討。梁のみ撤去時は残る丸柱の安定を確認。
- サイン内部の照明・電源配線、屋根下の照明・配線は事前に切離し。
- 高所作業（A 天端 H≧7m 想定）。高所作業車／足場、道路使用・歩道養生、営業中の車両移動を確認。
- 石綿含有建材（成形板・シーリング等）の事前調査結果を確認のうえ着手。撤去材は分別・横込・搬出・処分。

#### 現調メモ（実測・所見）

### ② 上空図（上から見る）

S = NTS

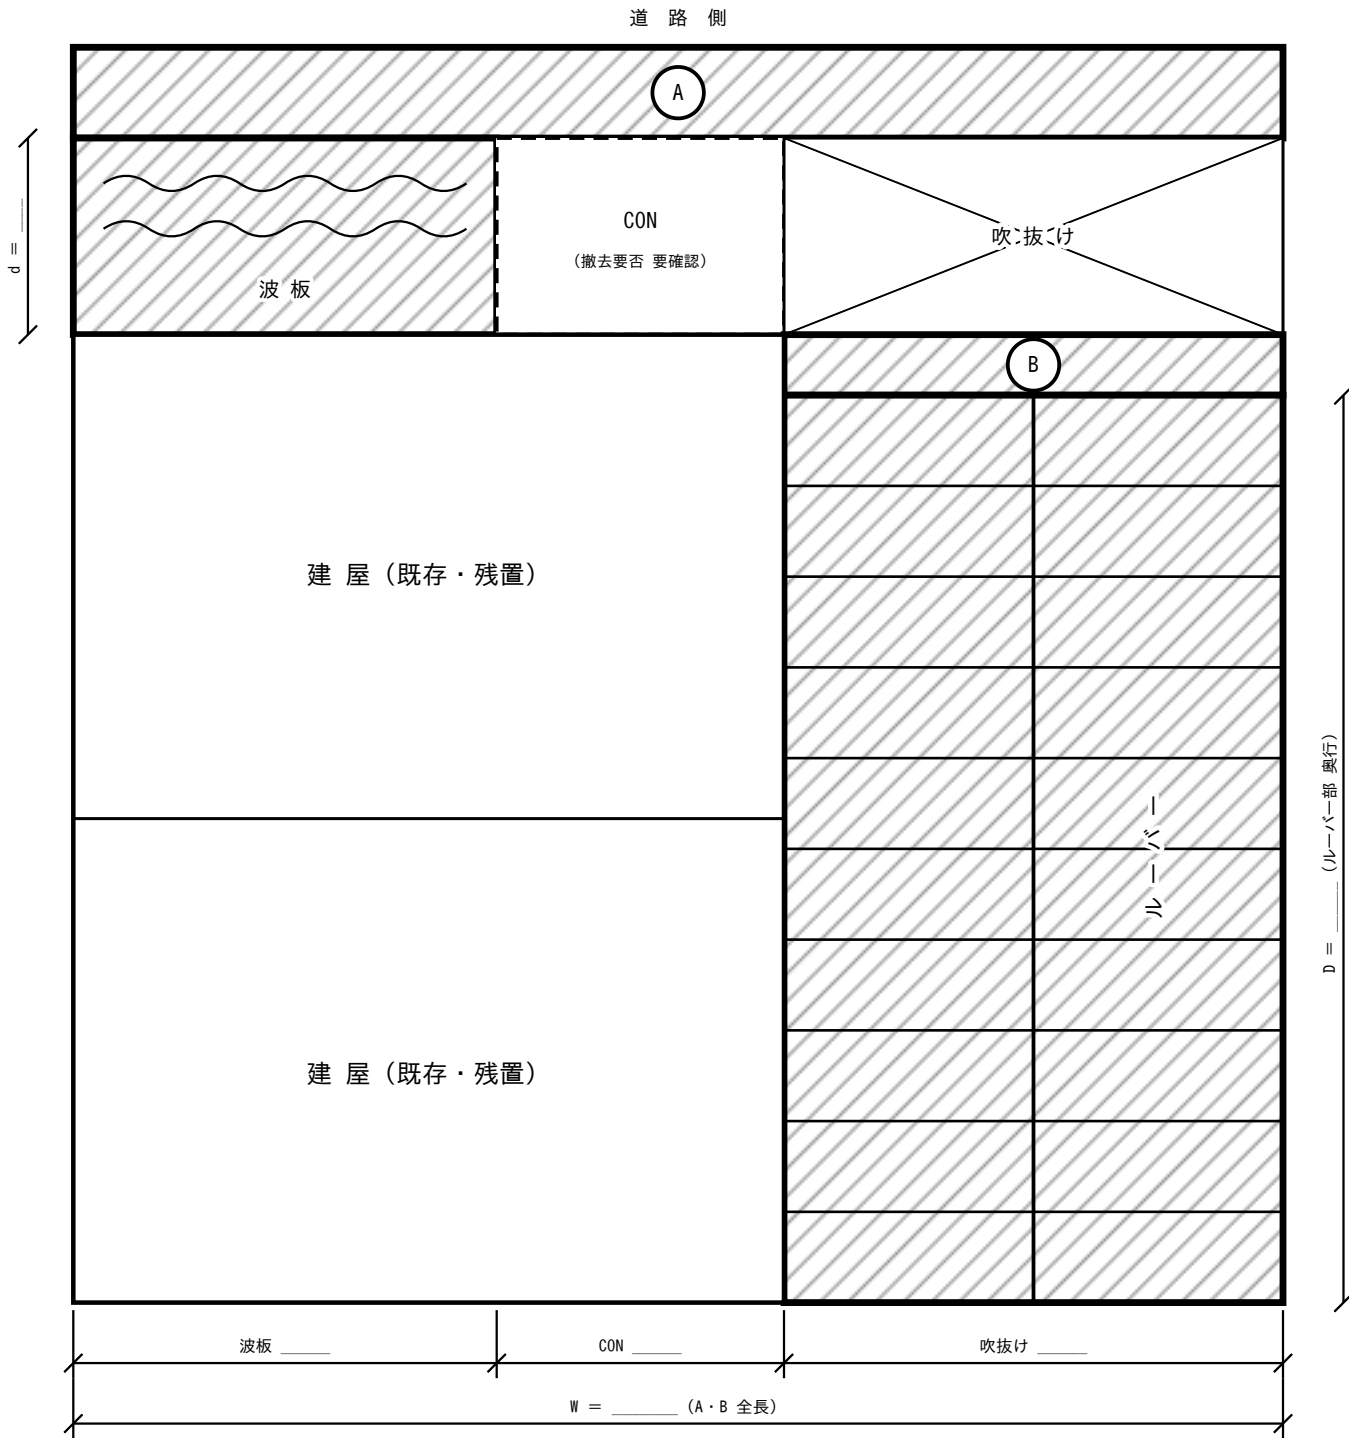

※ 手描きスケッチ（上から）をもとに作図。各部の寸法・区分は現地実測により確定。

※ 吹抜け部は撤去なし。CON 部・ルーバー部の撤去要否は現地でお客様と確認のこと。

※ 波板部・ルーバー部は B（中段梁）と一体で撤去する想定。

#### B 内訳（面積 記入欄）

波板 \_\_\_\_ × \_\_\_\_ = \_\_\_\_ m<sup>2</sup>

CON \_\_\_\_ × \_\_\_\_ = \_\_\_\_ m<sup>2</sup>

ルーバー \_\_\_\_ × \_\_\_\_ = \_\_\_\_ m<sup>2</sup>

吹抜け \_\_\_\_ × \_\_\_\_ = \_\_\_\_ m<sup>2</sup>

B 梁 全長 = \_\_\_\_ m

A 梁 全長 = \_\_\_\_ m

#### 撤 去 範 囲 図（現地調査用）

|                       |                            |                |  |
|-----------------------|----------------------------|----------------|--|
| 工事名                   | 車寄せ サイン梁・中段梁＋屋根 撤去工事（仮称）   |                |  |
| 所在地                   | 神奈川県横浜市都筑区茅ヶ崎南 3-23-5      |                |  |
| 建 物                   | 信和ホームズ㈱ 社屋 車寄せ（写真サイン表記による） |                |  |
| 現調日 2026/09/02（水）9:00 |                            | 作成日 2026/09/01 |  |
| 縮尺 NTS                | 用紙 A3                      | 図番 01（rev.2）   |  |